
SECTION A-A

SCALE 1:50 @ A3 (LOOKING EAST; JOGS WEST AT THE PUMP ROOM TO CUT ITS DOORS)

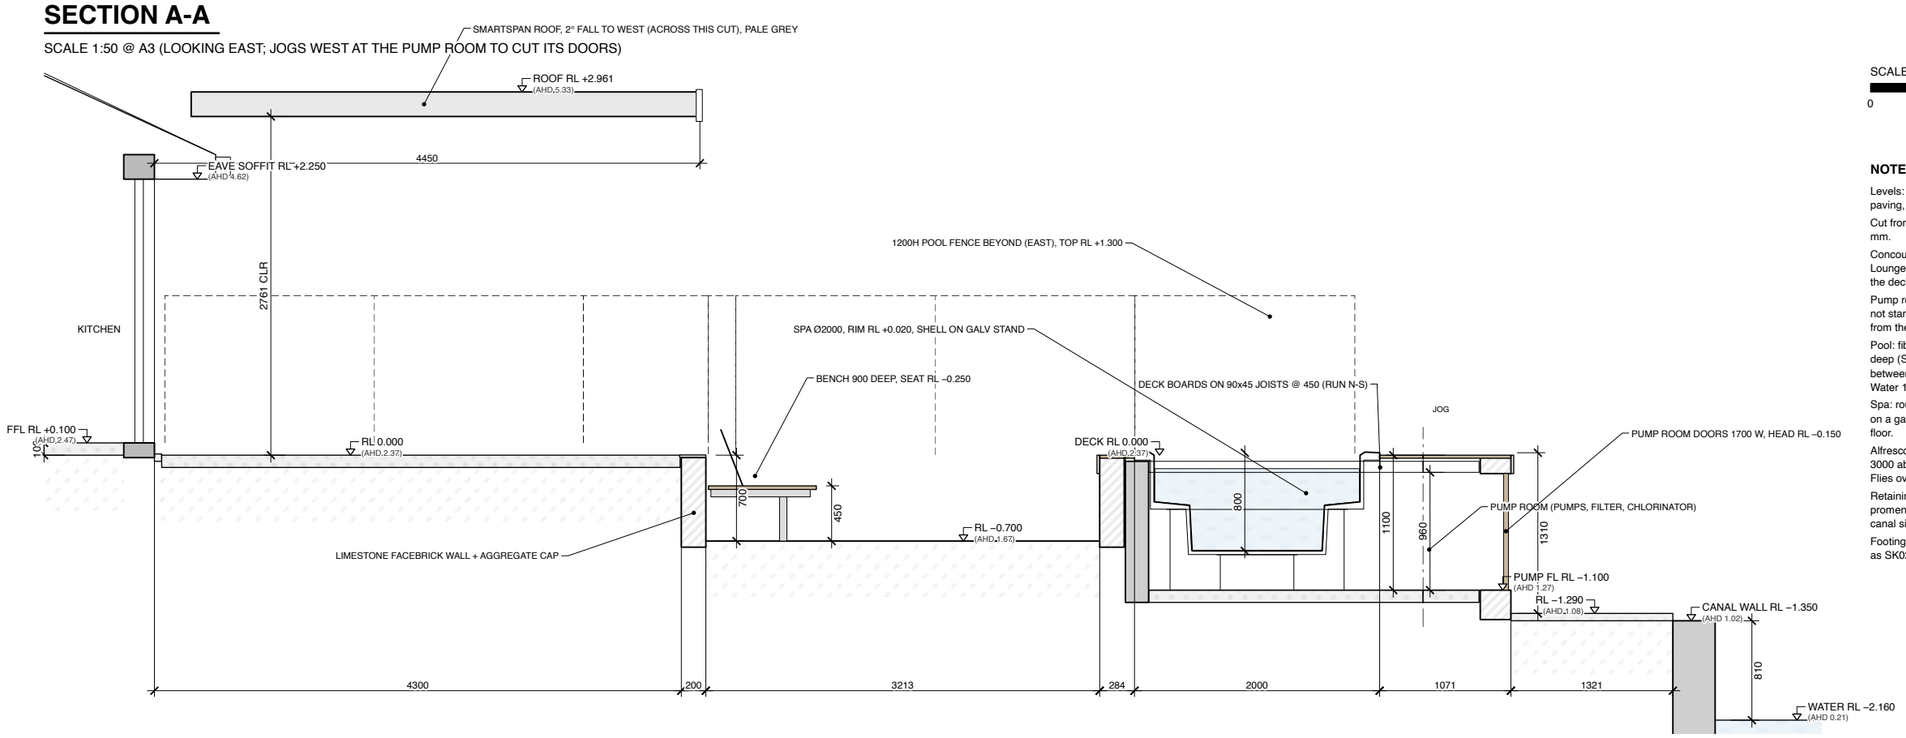

SCALE 1:50 @ A3

0 0.5 1 2 3 4 m

NOTES

Levels: RL 0.000 = AHD 2.37 (existing rear paving, SK02's datum). House FFL RL +0.100.

Cut from the 3D model's geometry. Heights in mm.

Concourse, alfresco and deck all RL 0.000. Lounge floor RL −0.700, 4 risers of 175 to the deck. Pump room floor RL −1.100.

Pump room: 960 clear under the joists (kneel, not stand), as SK02's levels. Doors only, from the promenade.

Pool: fibreglass, 1000 shallow (N) to 2000 deep (S) from coping top; floor falls between 3.0 and 5.4 m from the shallow end. Water 150 below coping.

Spa: round 2000, rim 20 above the deck, shell on a galvanised stand off the pump room floor.


Alfresco roof: Stratco Smartspan at 2°, top 3000 above paving at the high (east) side. Flies over the house gutter on brackets.

Retaining wall to promenade: 1310 from promenade to cap (the pool barrier on the canal side; see A3-03).

Footings, drainage (PVC drain from the lounge, as SK02) and structure by others.

SECTION B-B

SCALE 1:50 @ A3 (LOOKING NORTH)

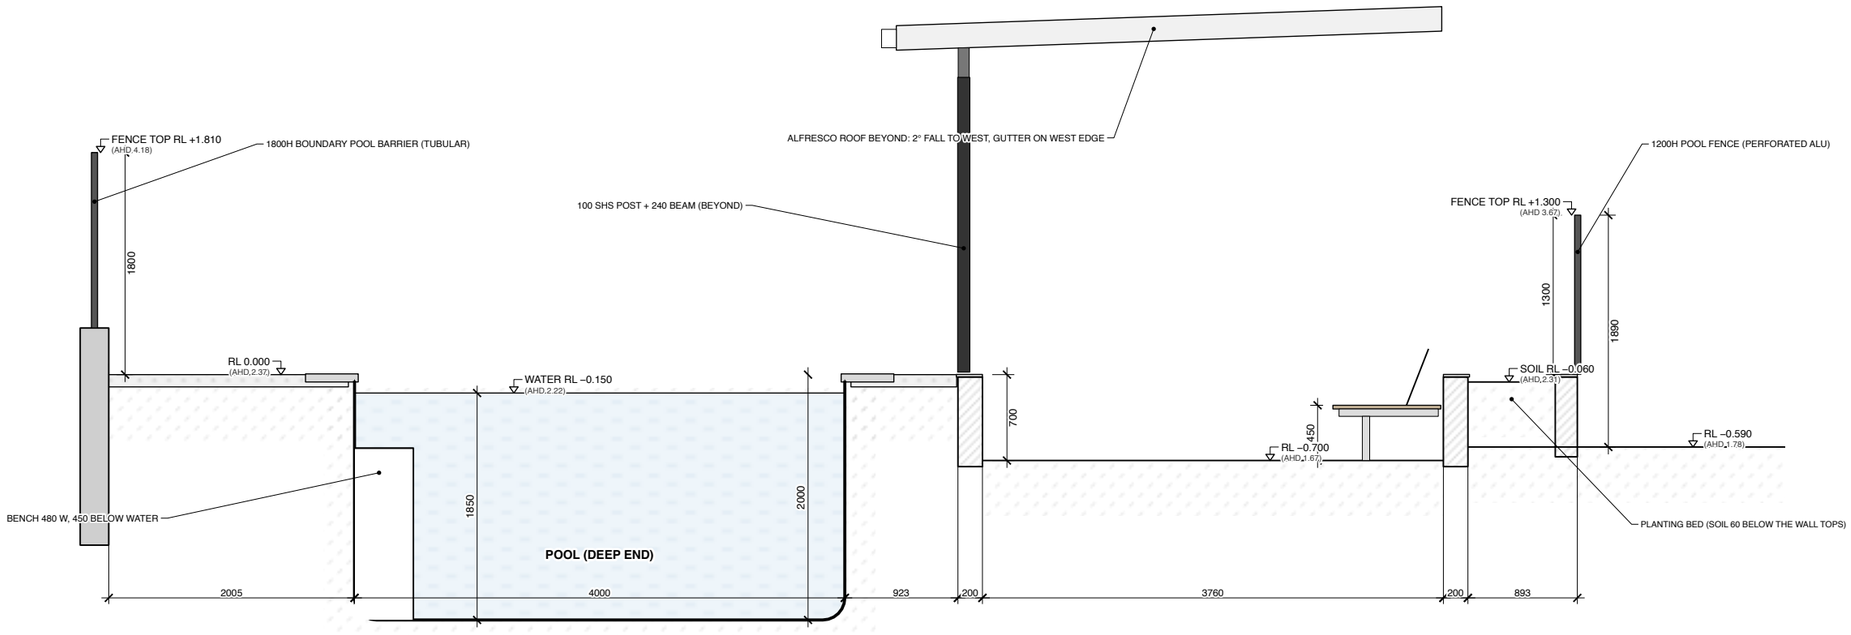

STATUS

Design intent from the 3D model.

For Bob Bruce to draw up.

NOT FOR CONSTRUCTION

Project:	PROPOSED POOL, SPA & ALFRESCO
Client:	CANN
Site:	35 KEEL RETREAT, PORT GEOGRAPHE

Sheet title	**SECTIONS A-A AND B-B**
Date	3 Nov 2026
Revision	B
Scale	1:50

SHEET

A3-02

Rev B