

ALFRESCO ROOF PLAN

SCALE 1:50 @ A3

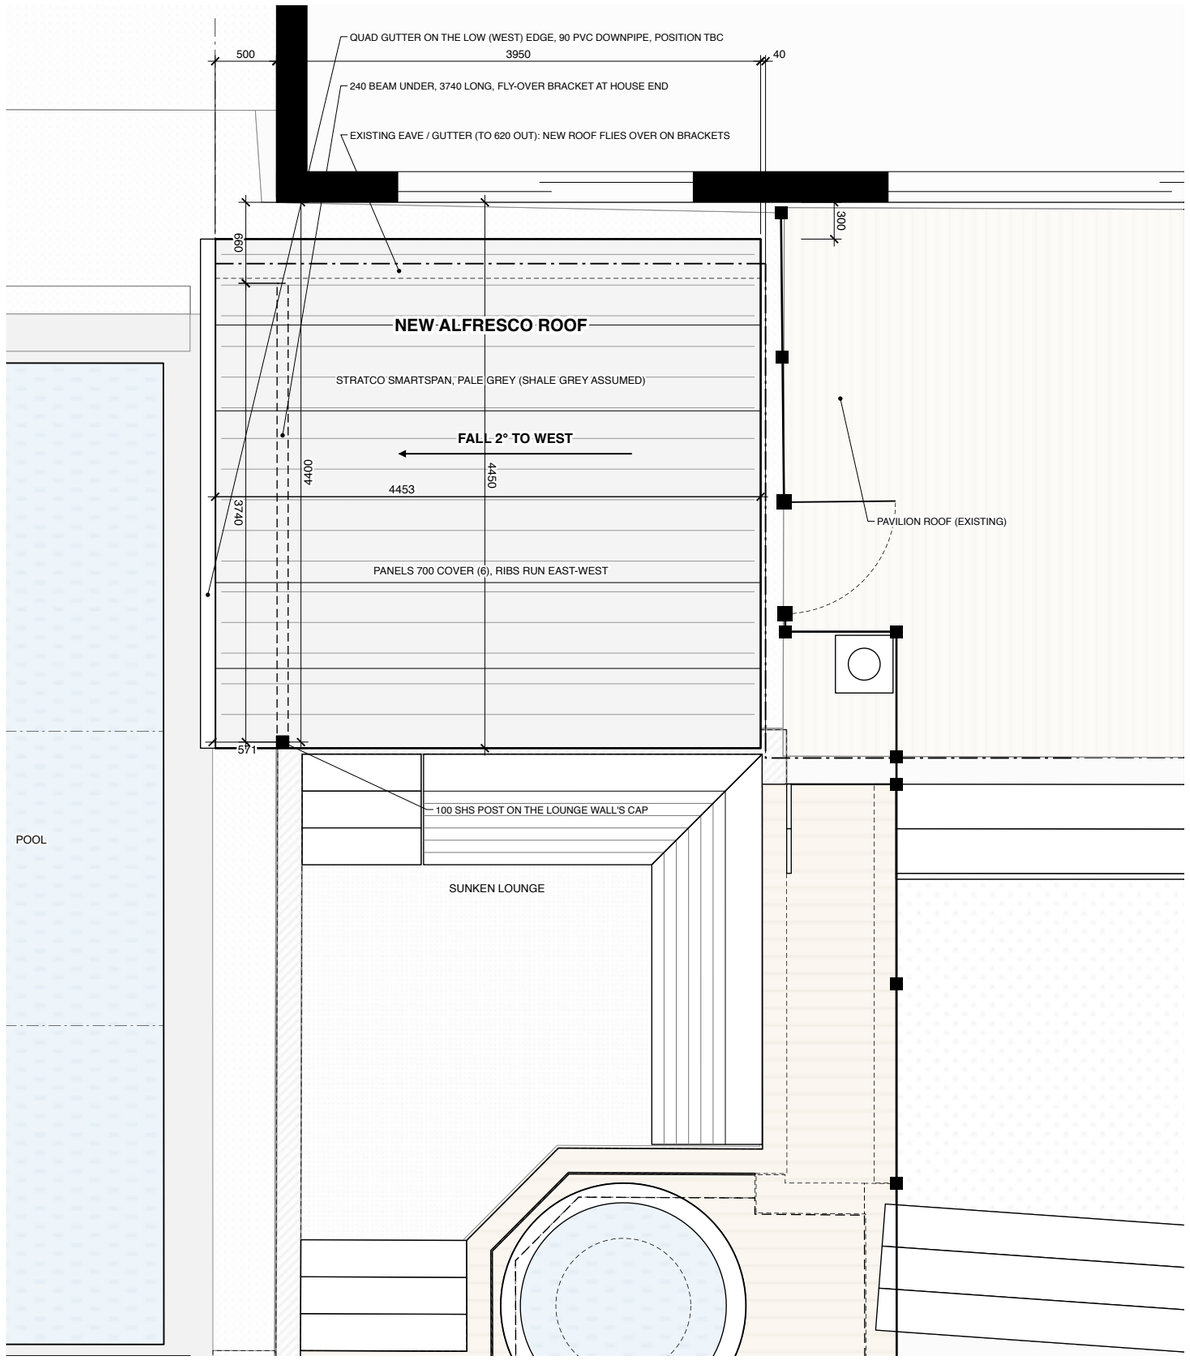

ROOF SECTION (EAST-WEST)

SCALE 1:50 @ A3, AT MID-DEPTH OF THE ROOF, LOOKING NORTH

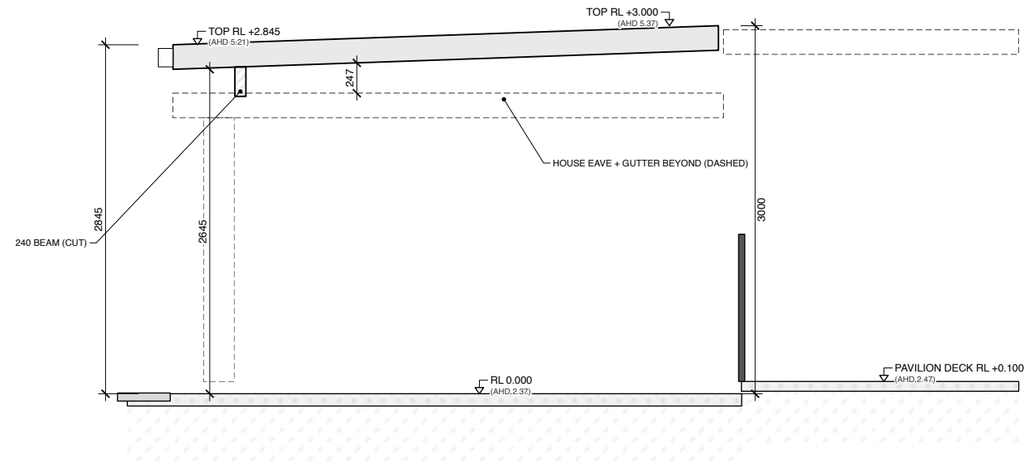

SCALE 1:50 @ A3



NOTES

Roof 4453 x 4150 plan, from 300 off the house wall to 4450 (south edge). West edge on the house's eave line (fascia face, 0 offset).

Fall 2° to the west. Top 3000 above the paving at the east (high) side, 2845 at the west. Ceiling flush, 2655 clear at the low side (model, at 300 in from the edge).

The house's rear gutter runs out to 620 from the wall, under the beam line: beams stop at 660 and need a fly-over bracket back to the house framing (or a post at the wall). SK02 runs the beam to the wall, through the gutter.

High (east) side meets the pavilion roof: assumed carried on the pavilion's column line (SK02 shows no post there). Engineer to confirm.

Drawn at 1:50 (not 1:100) so the 4.45 m roof is legible; the 1:100 context is on A3-01.

Post layout: one post at the roof's south-west corner (1 x 100 SHS post, beams 240 deep as modelled; sizes not engineered). Rafters 140x35 at 900 per the estimate.

STATUS

Design intent from the 3D model.

For Bob Bruce to draw up.

NOT FOR CONSTRUCTION

Project:	PROPOSED POOL, SPA & ALFRESCO
Client:	CANN
Site:	35 KEEL RETREAT, PORT GEOGRAPHE

Sheet title	**ALFRESCO ROOF PLAN**
Date	21 Oct 2026
Revision	A
Scale	1:50

SHEET

A3-04

Rev A