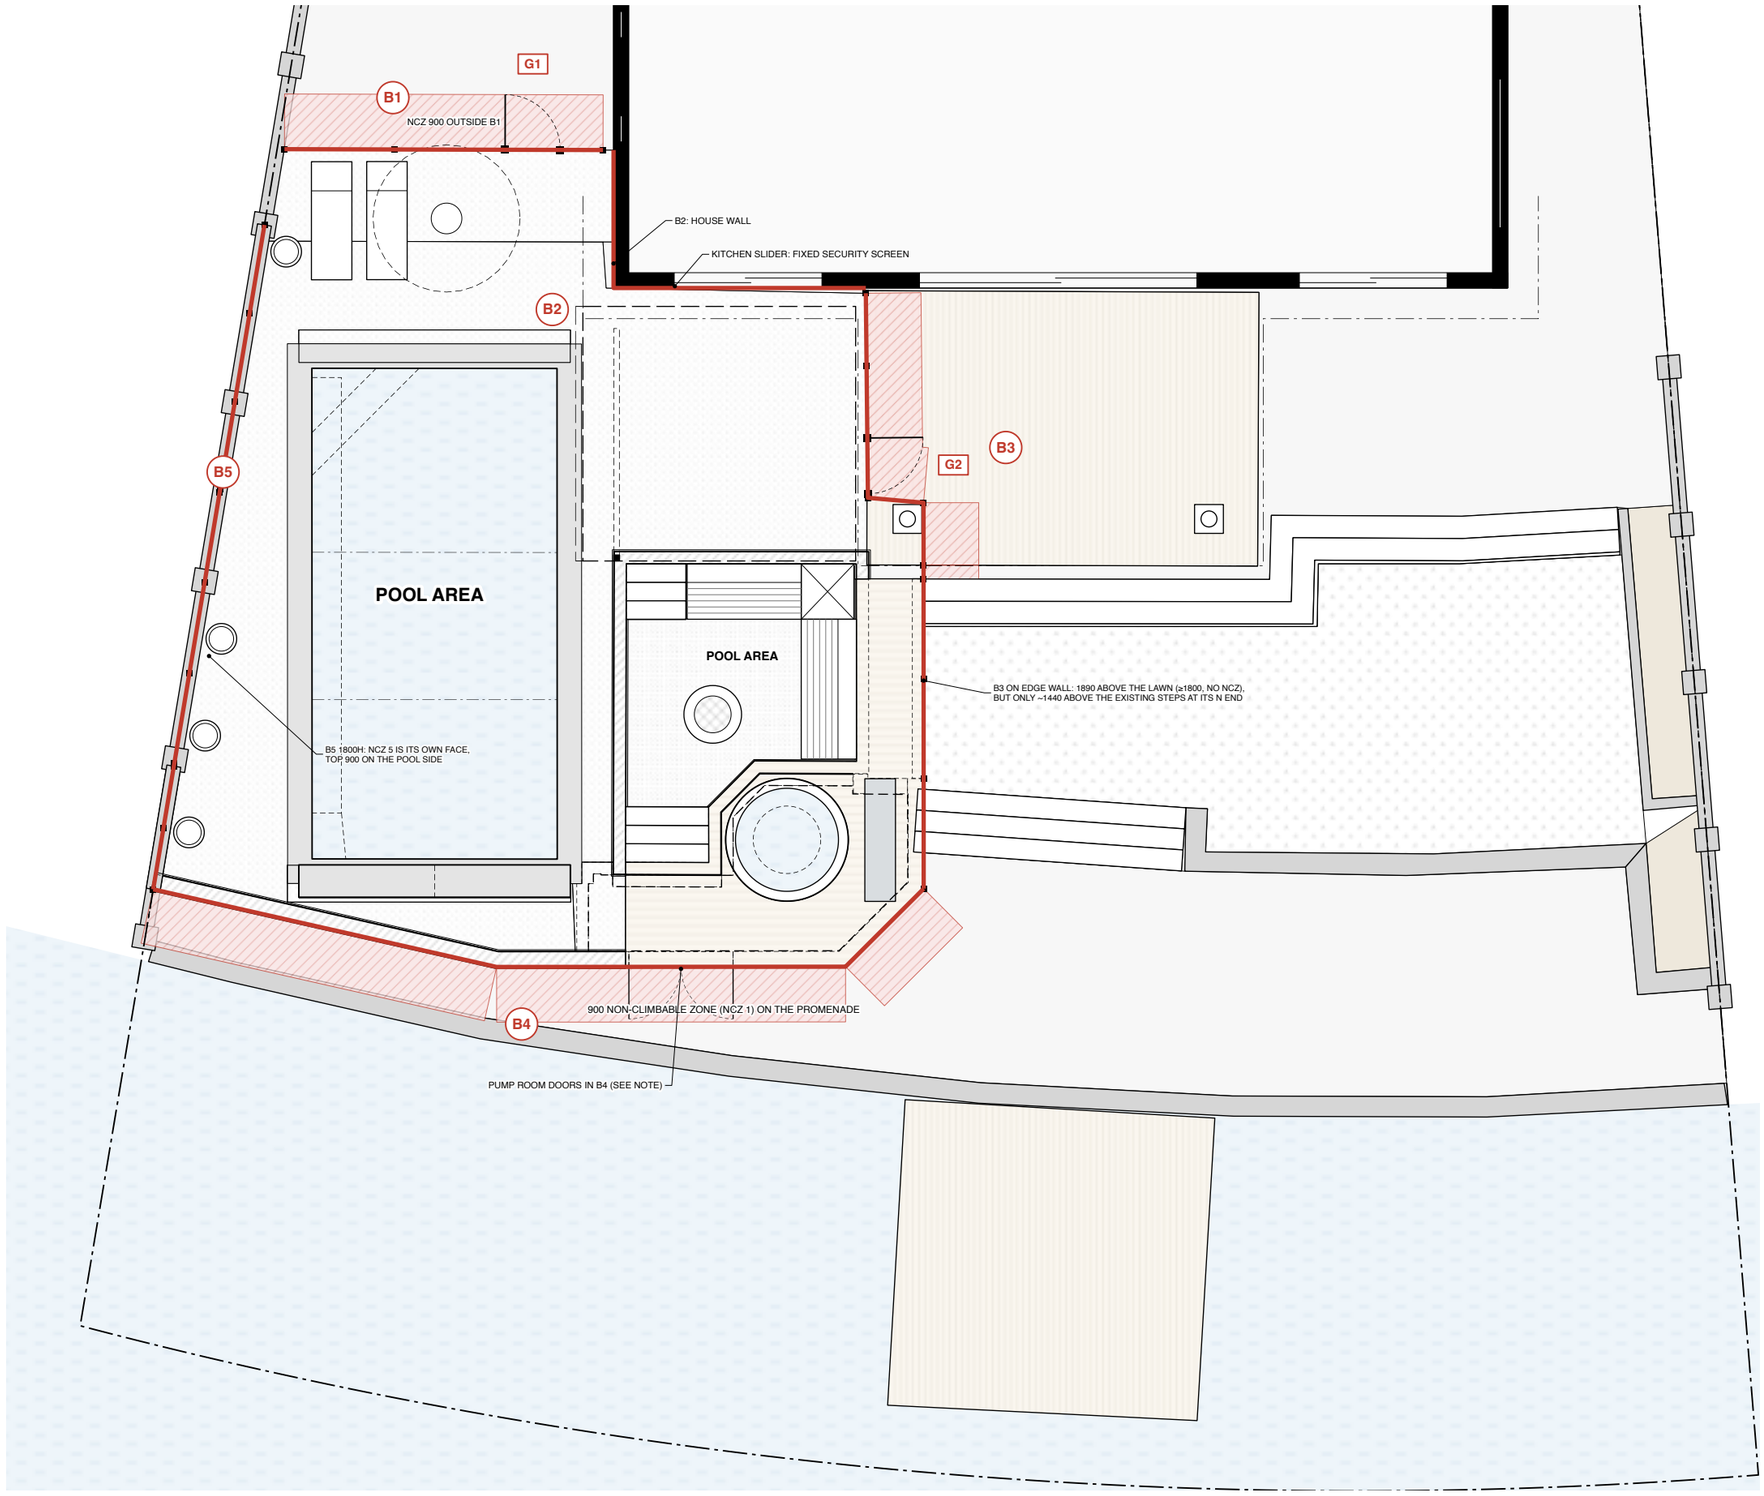


POOL BARRIER PLAN

SCALE 1:100 @ A3

N

SCALE 1:100 @ A3

0 1 2 3 4 5 10 m

BARRIER SCHEDULE

B1 Pool fence, perforated aluminium (charcoal). Height above the ground outside: 1240 mm, top RL +1.250.

B2 House walls (existing); kitchen slider with fixed security screen. Full-height wall.

B3 Pool fence, perforated aluminium, on the deck edge / edge wall. Height above the ground outside: 1200 to 2590 mm, top RL +1.300.

B4 Limestone retaining wall + cap (terrace wall). Height above the ground outside: 1310 mm, top RL +0.020.

B5 West boundary fence (tubular), poolside option. Height above the ground on the pool side: 1800 mm, top RL +1.800.

G1 Gate 900 wide in B1, 1250 high: self-closing and self-latching, swings out, away from the pool (arc shown).

G2 Gate 910 wide in B3, 1200 high: self-closing and self-latching, swings out, away from the pool (arc shown).

NOTES

Heights are from the model: barrier top minus the ground 350 mm outside it, every 250 mm along each run (range shown). WA Rules for Pools and Spas (2025): 1200 min. on the outside, 1800 for the boundary (poolside option).

Shaded: the 900 non-climbable zone (NCZ 1) outside barriers under 1800. Keep it clear of anything climbable: pots, furniture, the BBQ, taps, ledges.

B2: the kitchen slider opens from the house into the pool area. A fixed security screen is to be fitted (estimate 7 Oct); SK02 also notes re-glazing it to pool requirements. Certifier to confirm.

B4: the retaining wall is the barrier on the canal side. Its face must stay smooth (no footholds). The pump room doors (1700 x 950, outward opening onto the promenade) sit in it under the deck: their outside face needs to be non-climbable too, and the pump room has no opening into the pool area.

Fence ends at the house: the model stops B1 170 mm and B3 90 mm short of the wall face. Close them to the wall (gaps under 100 mm).

The pavilion's pillar is inside the fence, 28 from it.

STATUS

Design intent from the 3D model.

For Bob Bruce to draw up.

NOT FOR CONSTRUCTION

Project:	PROPOSED POOL, SPA & ALFRESCO
Client:	CANN
Site:	35 KEEL RETREAT, PORT GEOGRAPHE

Sheet title	**POOL BARRIER PLAN**
Date	21 Oct 2026
Revision	A
Scale	1:100

SHEET

A3-03

Rev A